4th Floor

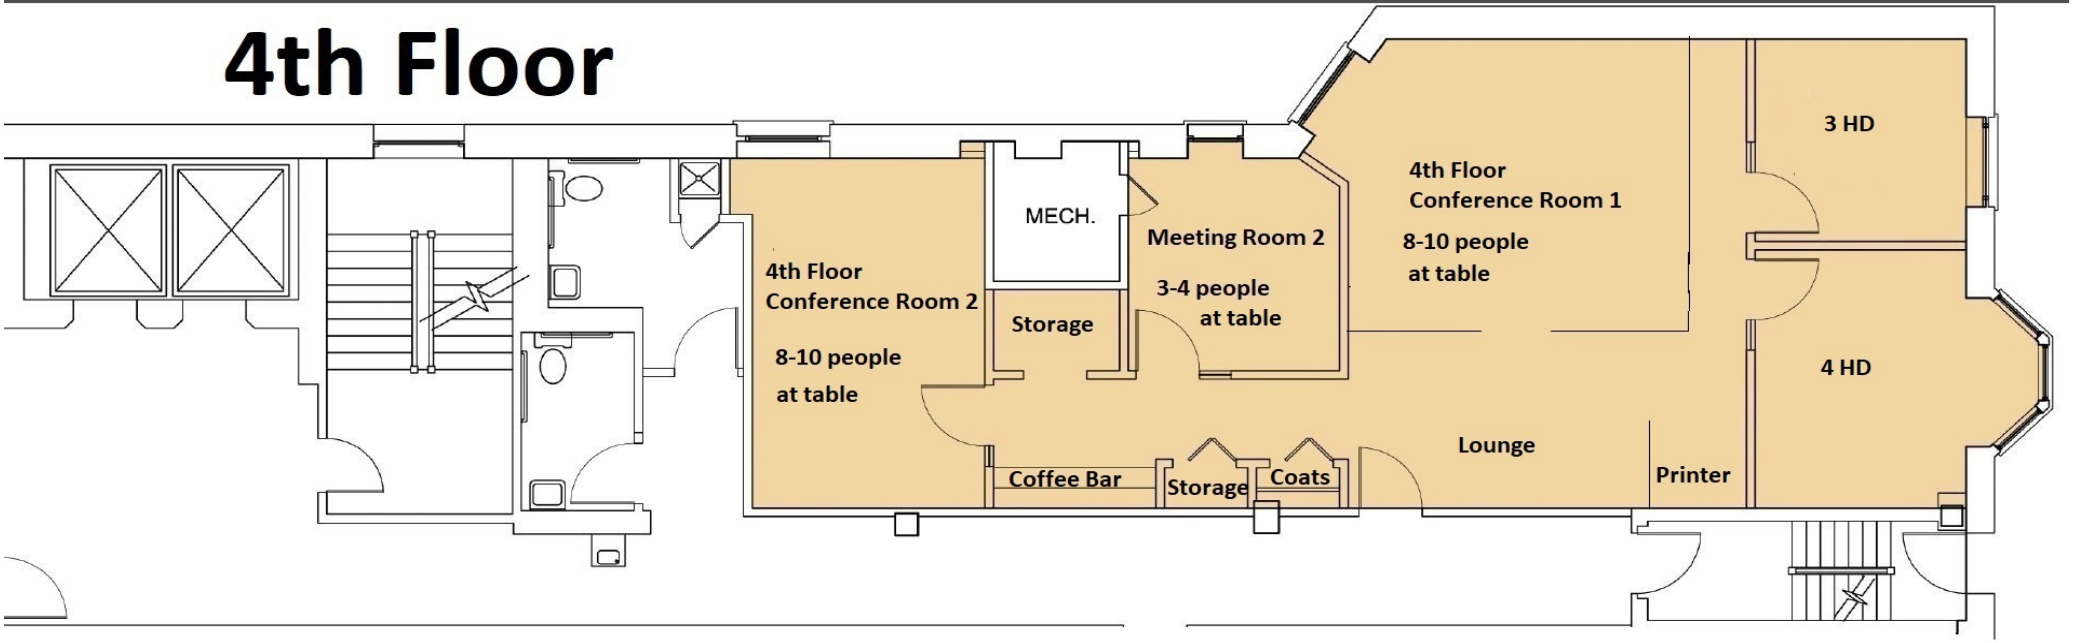

7th Floor

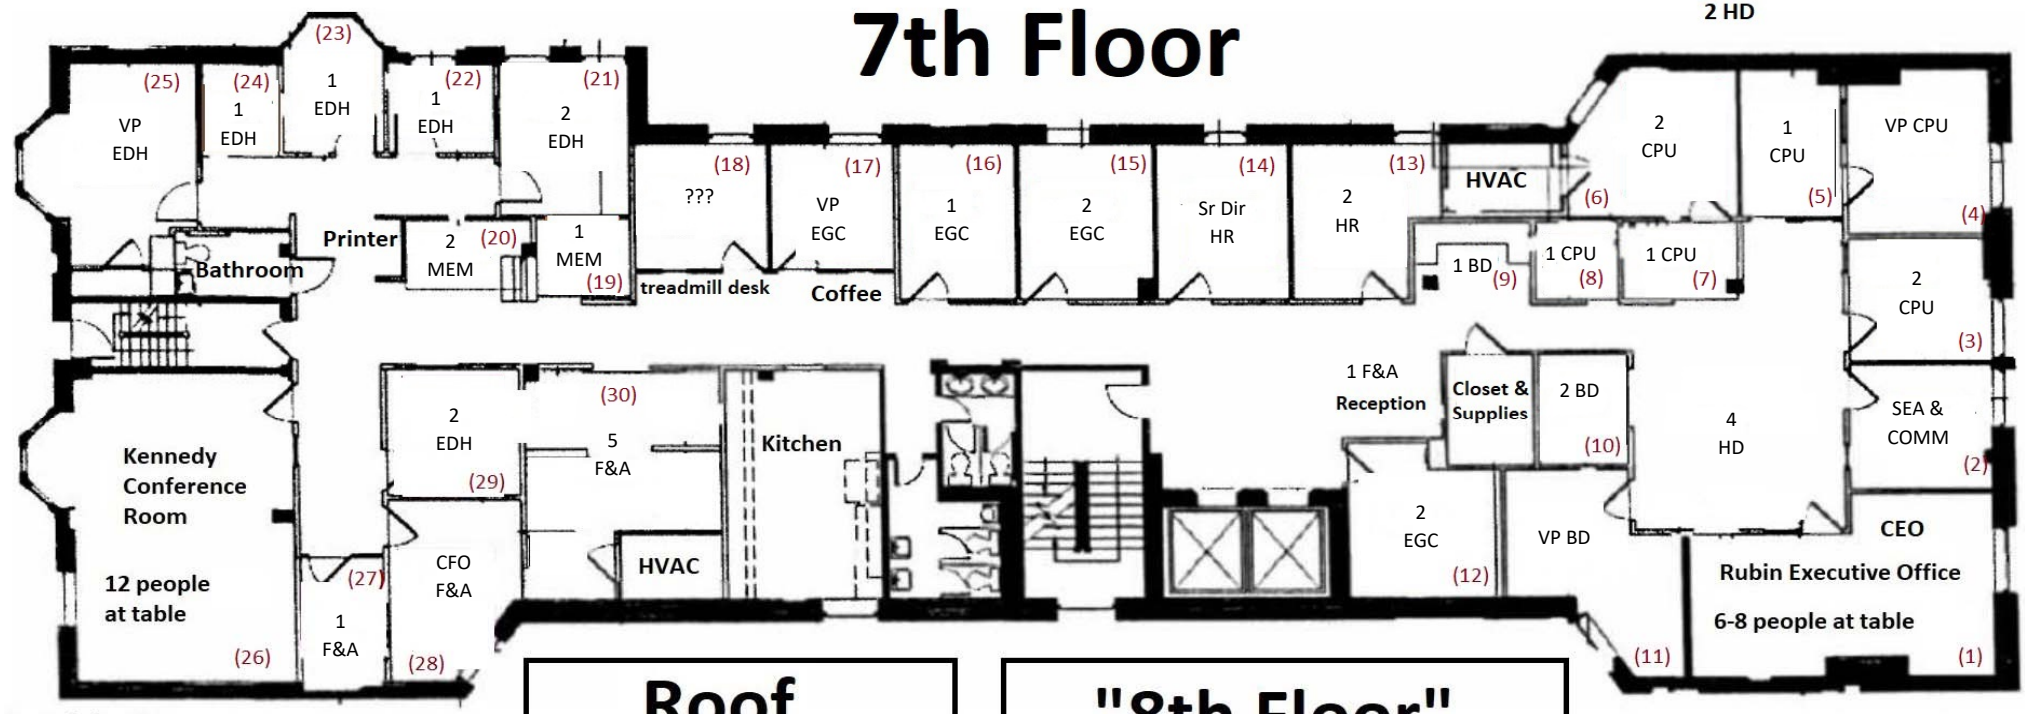

Not including VPs
6 EDH
2 MEM
7 CPU
5 EGC
6 F&A
2 HR
3 BD
1 COM
6 interns

Roof

Roof Top Deck

12-15 people
at tables

"8th Floor"

Lounge

6-8 people
with seats